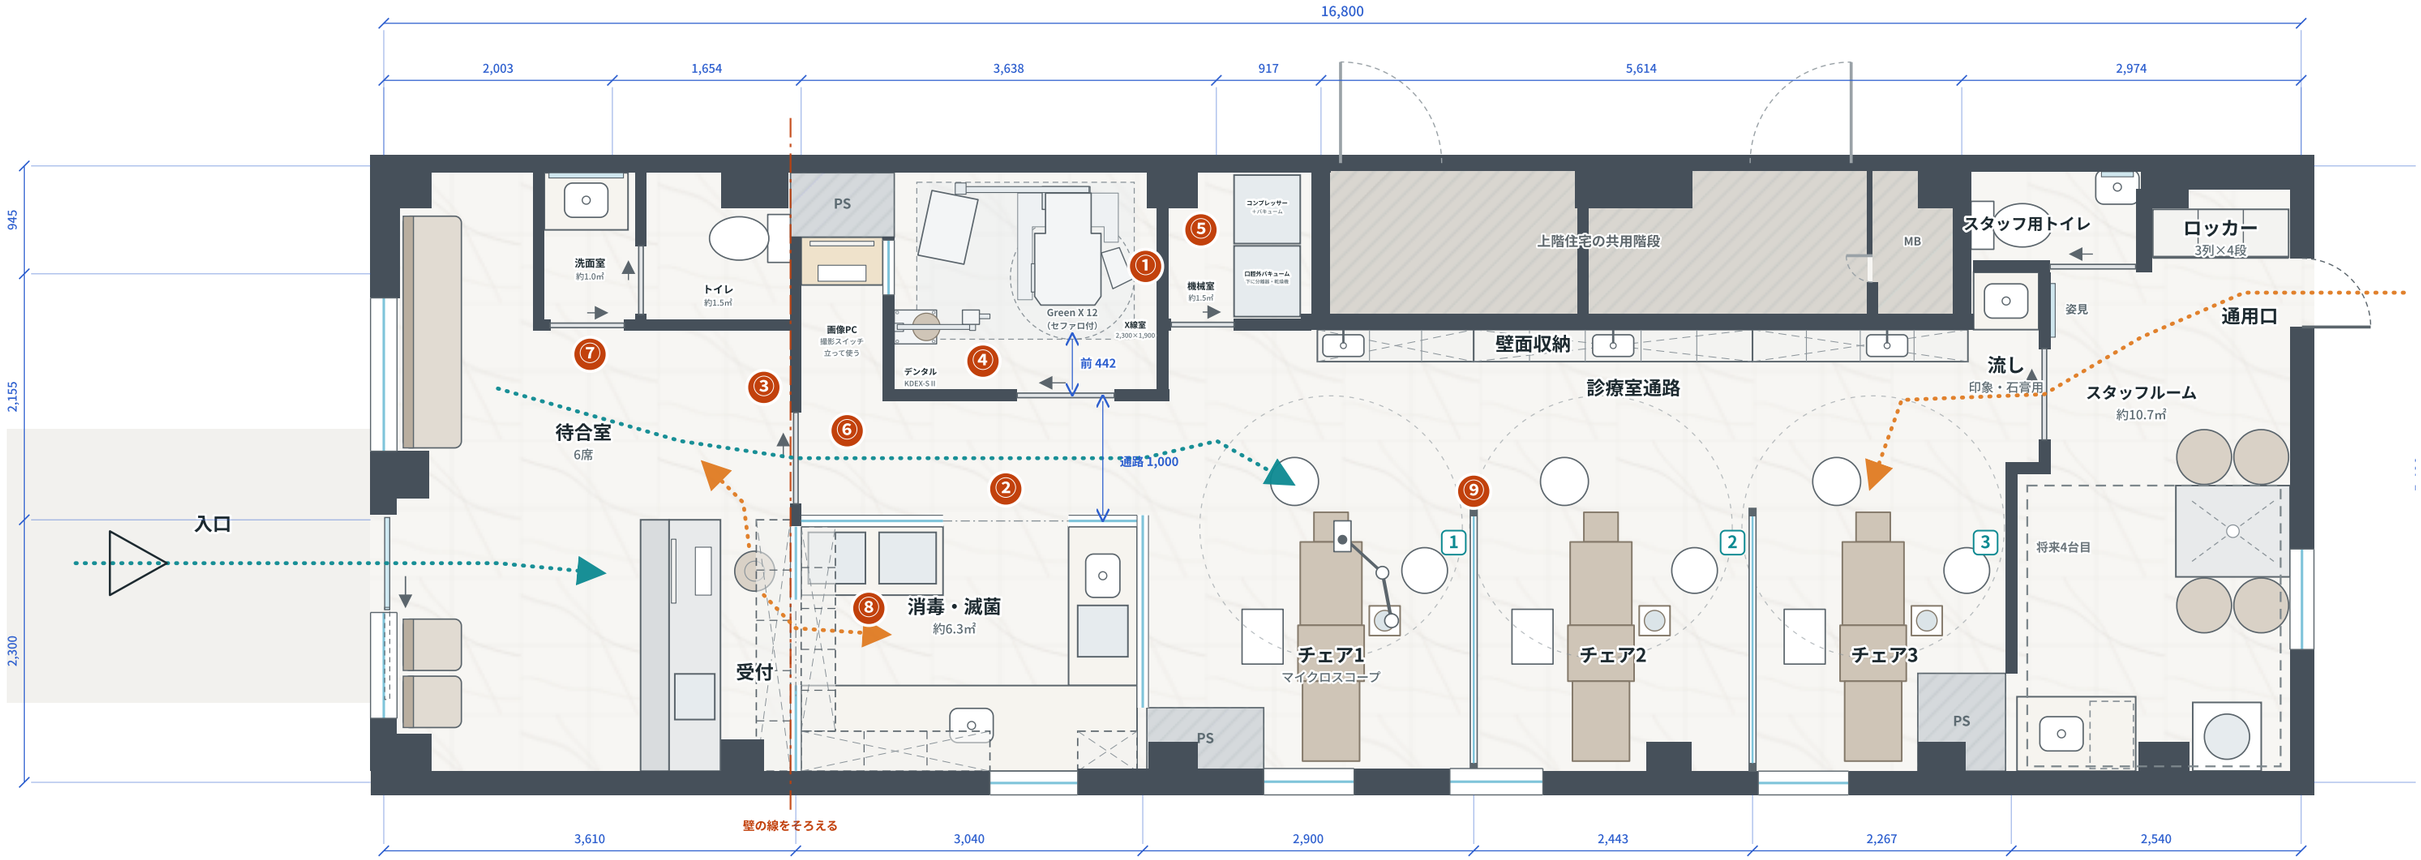


翔案5からの変更点

1. エックス線撮影室の奥行きを1.44m→1.90mに、幅は2.3mに（推奨2,300×1,900・約4.3㎡）。CTはバテック Green X 12（セファロ付・セファロは左）。回る範囲の前から壁まで約44cm
2. 通路の幅1.0mを残すため、消毒・滅菌の前の壁を約0.41m下げた（消毒・滅菌 約7.5㎡→約6.3㎡）
3. 診療室入口も、通路に合わせて約0.56m下へ（幅0.8m）
4. デンタル（KDEX-S II）は背中を左の壁につけ、患者さんは右を向いて座る。廊下側の壁から約40cm離し、頭の左右に約54cmずつあけた。セファロを撮るときはアームをよける
5. 機械室はX線室の右に、縦積みでコンパクトに（約1.5㎡）。コンプレッサーとバキュームを縦に積み、口腔外バキューム本体の台の下に分離器と乾燥機。空いた分で通路の入口を広げた
6. 画像PCと撮影スイッチは元の機械室の右半分（PSの下・約1.0㎡）。イスなしで立って使う（台の高さ約1,000）。扉なしで通路から入る。X線室の確認用の窓もこちらの壁に。トイレから受付までの壁の線をまっすぐにそろえた
7. 患者用トイレは手洗いなし（約1.5㎡・便器はPS側）。洗面台（洗口・手洗い）は個室の洗面室（約1.0㎡）にし、トイレへは洗面室から入る。待合は6席
8. 消毒・滅菌の窓側の作業台を奥行き600→750に。受付からの通り口は約10cm上へずらした（幅0.75mのまま）
9. チェアの間のガラス間仕切りに枠をつけた（ぶつかっても割れにくく）

- 患者さんの動線
- スタッフの動線
- ガラス間仕切り（H1,600・下から1.4mすりガラス・枠つき）
- 壁・柱
- [1] ブース番号（ガラスに彫刻）
- ガラス壁（天井まで・下から1.3mすりガラス）
- 床：白の大理石（入口から全体）

翔案6B（X線室 推奨寸法）

翔案5から：X線室を推奨寸法 2,300×1,900 に・機械室と水まわりも見直し

中葛西の建物 16,800×5,400（壁芯）／2026.11.04／寸法 mm

0 1 2 3 4 5 m

共通：マイクロスコープはチェア1に取り付け（床置きなし）
共通：診療室・消毒滅菌・スタッフルームの窓は高窓（床から約2.0〜2.4m）
点線の四角は吊戸棚・上部収納（床から約1.5m以上）