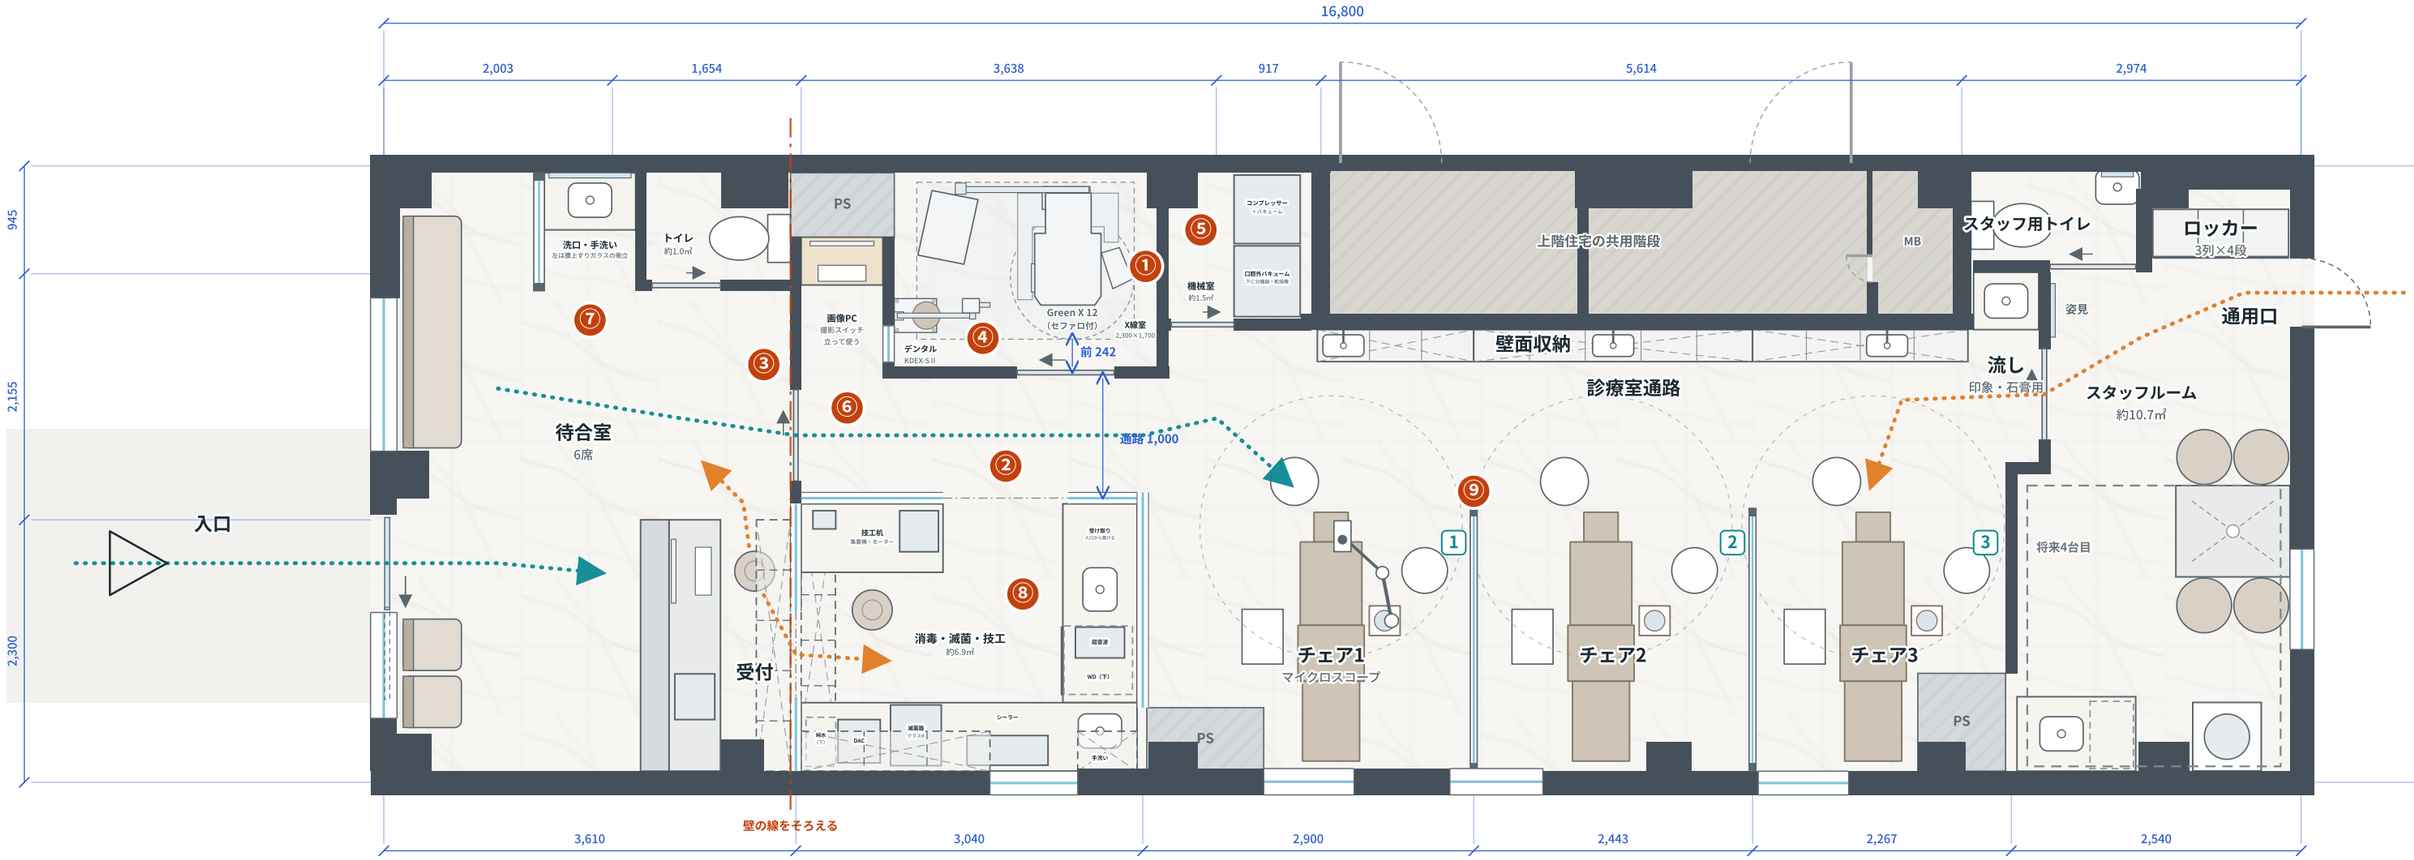


翔案5からの変更点

1. エックス線撮影室の奥行きを1.44m→1.70mに、幅は2.3mに（最低2,000×1,700・約3.9㎡）。CTはバテック Green X 12（セファロ付・セファロは左）。回る範囲の前から壁まで約24cm
2. 通路の幅1.0mを残すため、消毒・滅菌の前の壁を約0.21m下げた（消毒・滅菌 約7.5㎡→約6.9㎡）
3. 診療室入口も、通路に合わせて約0.36m下へ（幅0.8m）
4. デンタル（KDEX-S II）は背中を左の壁につけ、患者さんは右を向いて座る。廊下側の壁から約30cm離し、頭の左右に約44cmずつあけた。セファロを撮るときはアームをよける
5. 機械室はX線室の右に、縦積みでコンパクトに（約1.5㎡）。コンプレッサーとバキュームを縦に積み、口腔外バキューム本体の台の下に分離器と乾燥機。空いた分で通路の入口を広げた
6. 画像PCと撮影スイッチは元の機械室の右半分（PSの下・約0.8㎡）。イスなしで立って使う（台の高さ約1,000）。X線室の確認用の窓は手前側に（デンタルの柱をよけて・幅約32cm）。トイレから受付までの壁の線をまっすぐに
7. 患者用トイレは手洗いなし（約1.0㎡・便器はPS側）。扉は待合側の引き戸（洗面のすぐ横）。洗口・手洗い（洗面台1つ）はトイレの外で、左は腰上すりガラスの衝立（高さ約1.8m）。待合は6席
8. 消毒・滅菌・技工の機材を汚れ→きれいの一方向に配置。使用済みトレーは入口のすぐ右（右カウンターの手前）に、入口から置ける。窓側カウンター（奥行60cm）：シーラー・クラスB滅菌器・DAC／左上：技工机
9. チェアの間のガラス間仕切りに枠をつけた（ぶつかっても割れにくく）

- 患者さんの動線
- スタッフの動線
- ガラス間仕切り（H1,600・下から1.4mすりガラス・枠つき）
- 壁・柱
- 1 ブース番号（ガラスに彫刻）
- ガラス壁（天井まで・下から1.3mすりガラス）
- 床：白の大理石（入口から全体）

翔案6A（完成案）

翔案5から：X線室を最低寸法 2,000×1,700 に・機械室と水まわりも見直し

中葛西の建物 16,800×5,400（壁芯）／2026.11.04／寸法 mm

0 1 2 3 4 5 m

共通：マイクロスコープはチェア1に取り付け（床置きなし）
共通：診療室・消毒滅菌・スタッフルームの窓は高窓（床から約2.0〜2.4m）
点線の四角は吊戸棚・上部収納（床から約1.5m以上）