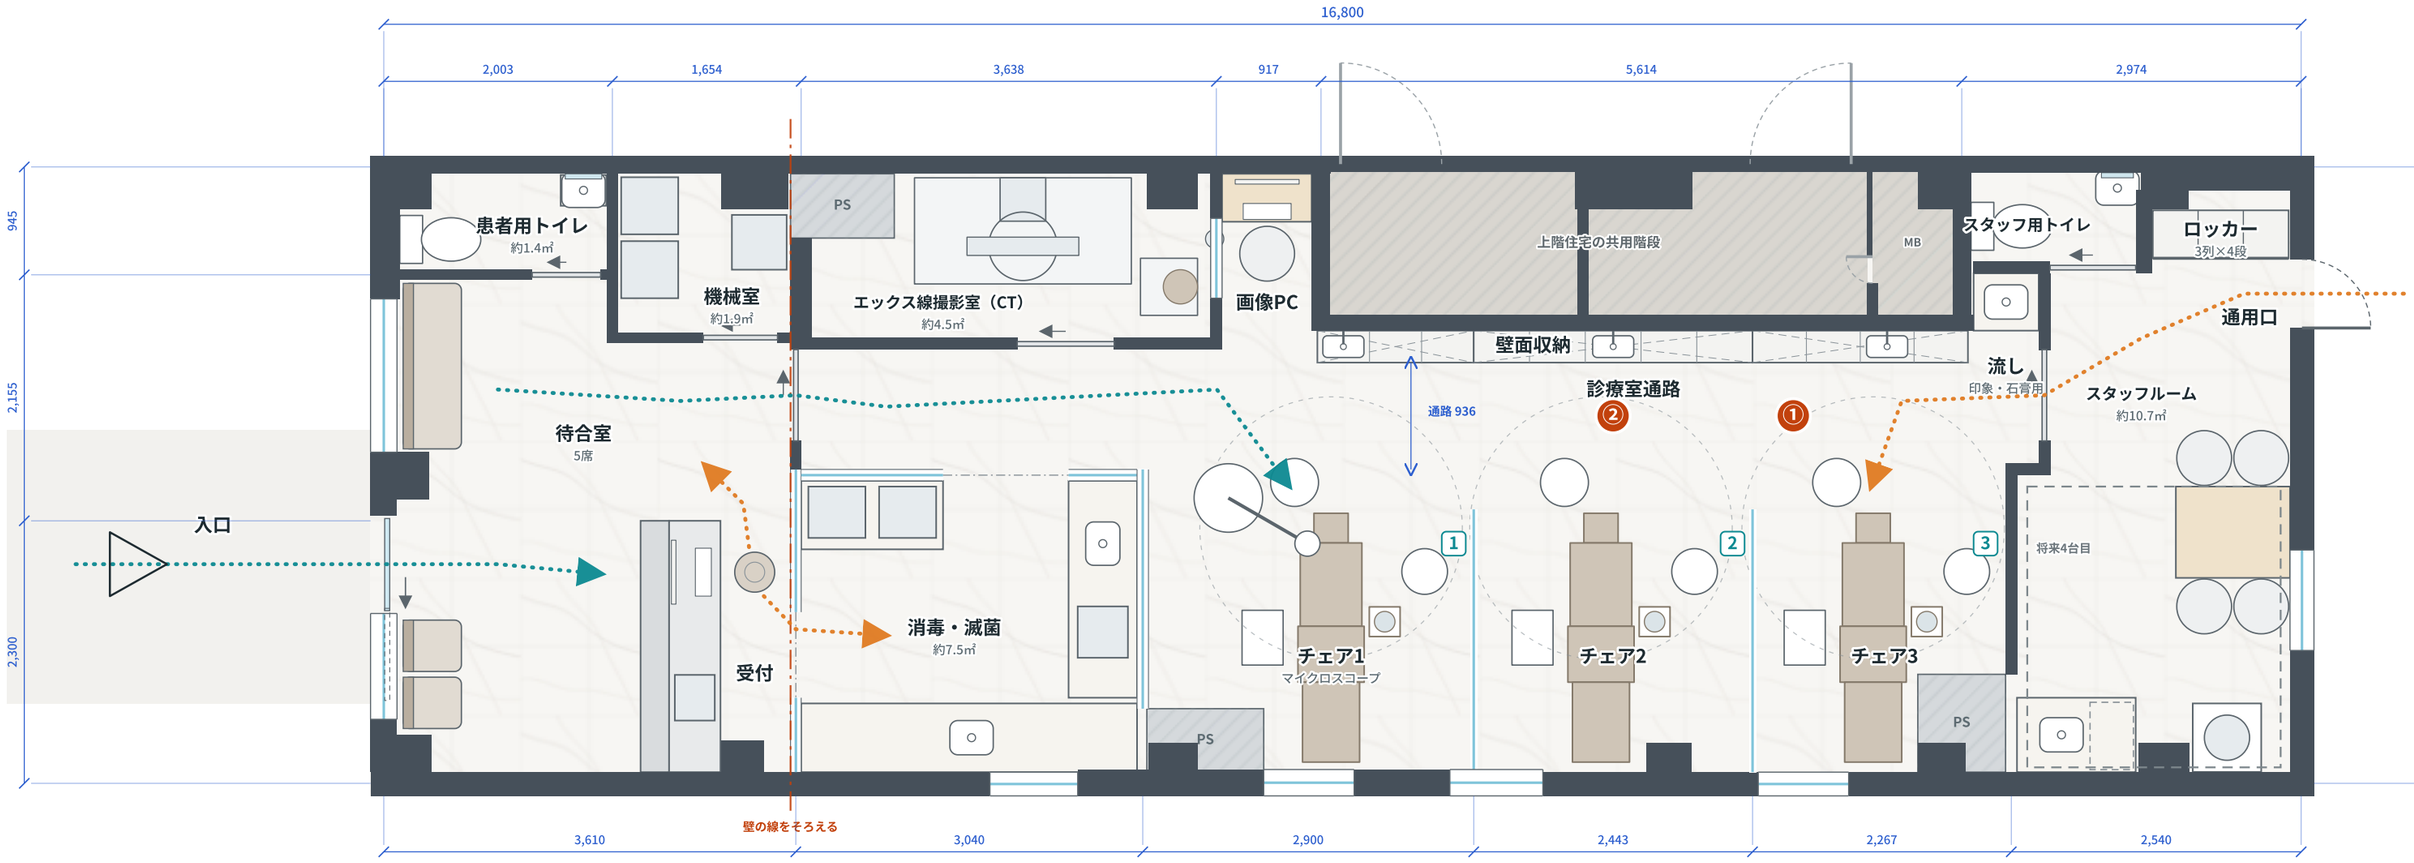


翔案2からの変更点

① チェアの頭側（通路の向かいの壁）に、床から天井までの収納（奥行き28cm）。下は収納、中ほどは作業台（高さ約85cm）、約1.55m〜天井も収納

② チェアごとに小さな手洗い（壁付けの水栓）。チェアの頭のすぐ後ろ

- 患者さんの動線
- スタッフの動線
- ガラス間仕切り（H1,600・下から1.4mすりガラス）
- 壁・柱
- 1 ブース番号（ガラスに彫刻）
- ガラス壁（天井まで・下から1.3mすりガラス）
- 床：白の大理石（入口から全体）

翔案4

翔案2から：チェアの頭側に床〜天井の収納・作業台と手洗い

中葛西の建物 16,800×5,400（壁芯）／2026.11.03／寸法 mm

0 1 2 3 4 5 m