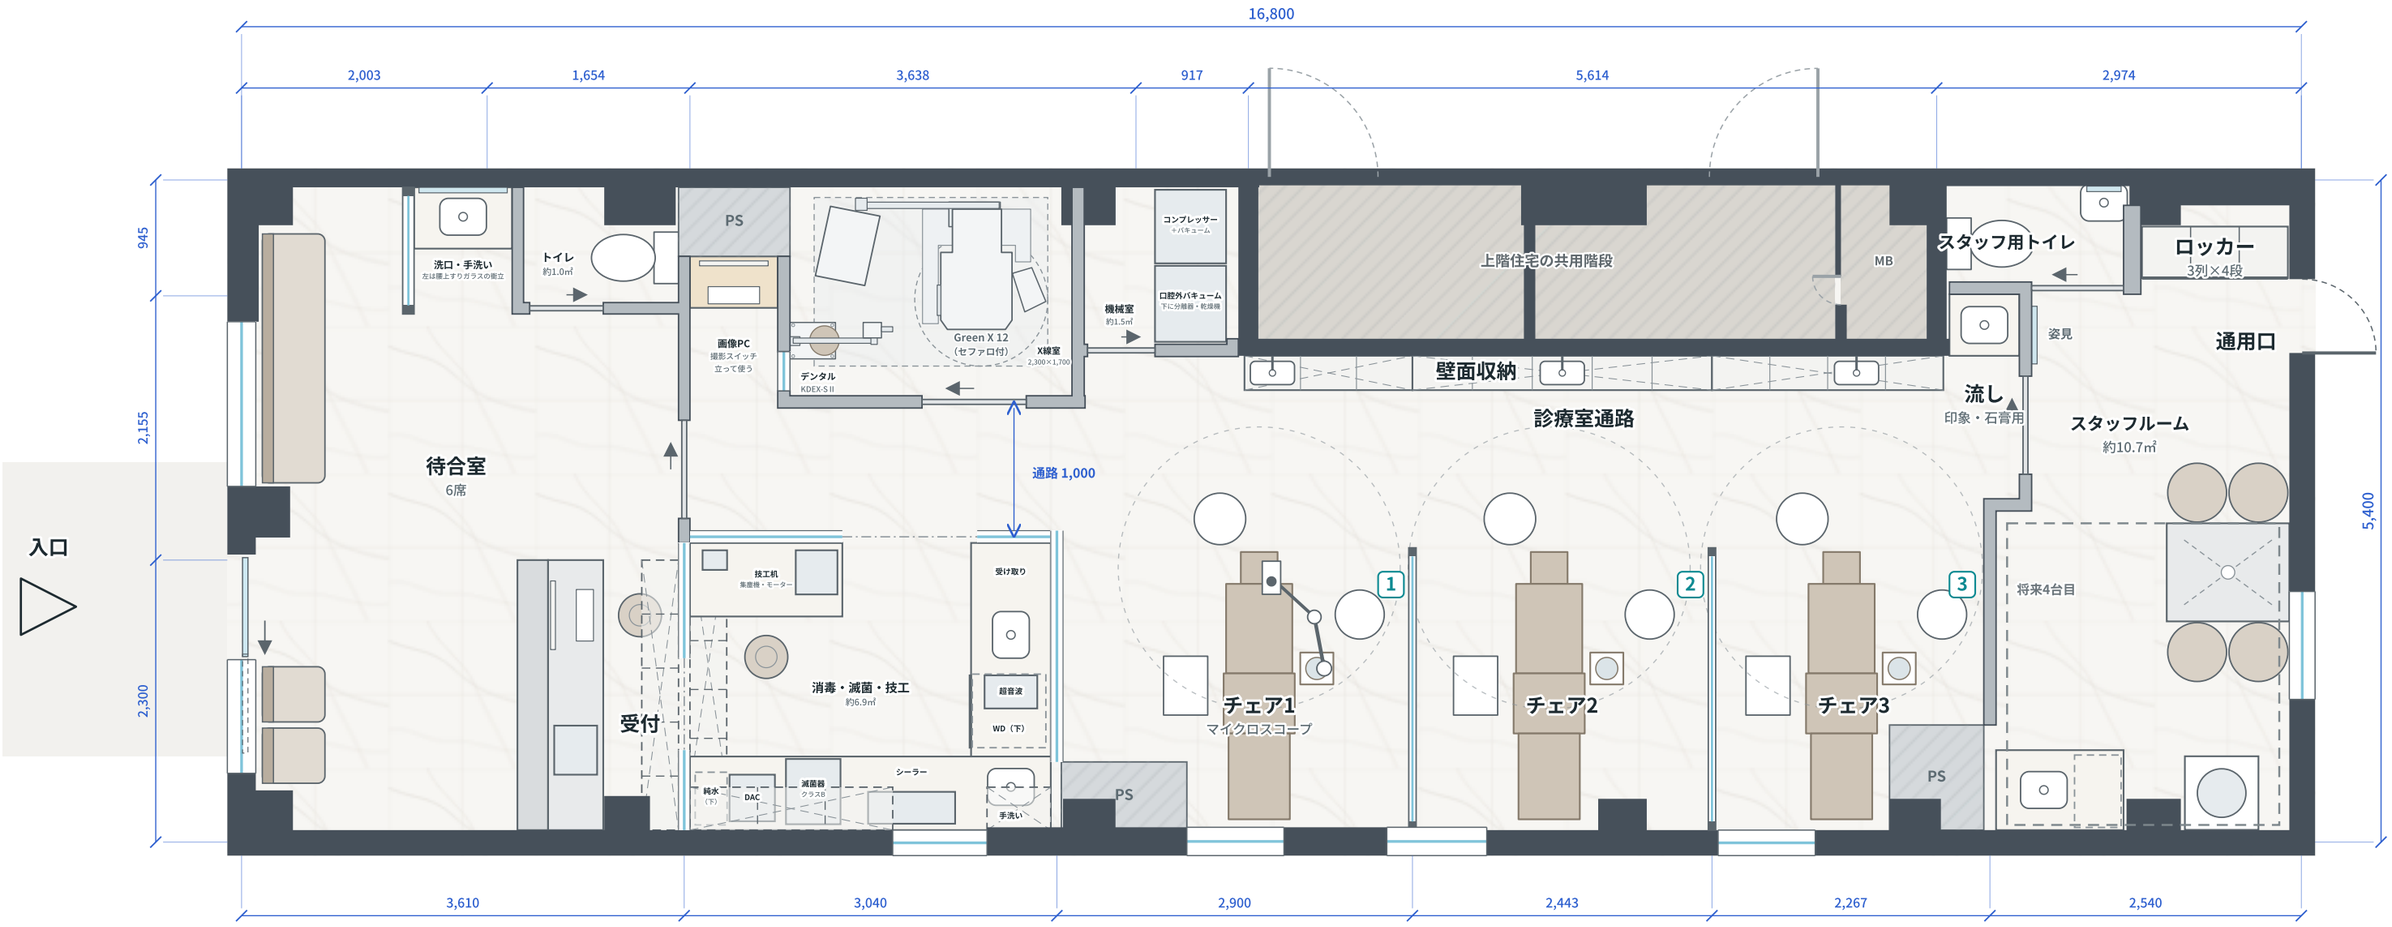


凡例

- 既存の壁・柱（躯体）
- 新設の壁
- ガラス壁（天井まで・下から約1.3mすりガラス）
- ガラス間仕切り（高さ約1.6m・下から約1.4mすりガラス・枠つき）
- 衝立（腰壁 約0.85m＋すりガラス 約1.8mまで）
- 吊戸棚・上部収納（床から約1.5m以上）
- 点線：カウンター下の機器・将来の配置
- PS・共用階段（既存・工事範囲外）
- 1 ブース番号（ガラスに彫刻）
- 床：白の大理石調（入口から全体）

注記

1. 本図は計画段階の平面図です。寸法は既存図面（16,800×5,400・壁芯）からの想定で、現地の実測で確定してください。
2. 天井高は2,600（仮）。床は入口から全体を白の大理石調とします。
3. エックス線撮影室の壁・扉・窓は放射線を遮へいします（鉛など・仕様は遮へい計算による）。撮影スイッチは室外に置きます。
4. ガラスは強化ガラスか合わせガラスとします。受付の後ろのガラス壁は床から約2.0mまでで、その上は吊戸棚です。
5. 診療室・消毒滅菌・スタッフルームの窓は高窓（床から約2.0〜2.4m）にする計画です。サッシの工事には管理組合・オーナーの承認が必要です。
6. マイクロスコープはチェア1に取り付けます（床置きなし）。
7. 給排水・電気・空調・換気・エア・バキュームなどの設備は、別図とします。

中葛西 歯科医院（仮称）内装工事

平面図　完成案

縮尺	1/50（A3）
日付	2026.11.04
建物	16,800×5,400（壁芯）
単位	mm

0　1　2　3　4　5　m