
A-01 仕上げ平面図・内装仕上表

中葛西 歯科医院（仮称）内装工事　計画段階の案（見積用）
もとにした案：翔案（2026.11.03）　縮尺：1/50（A3）　作成：2026.11.03

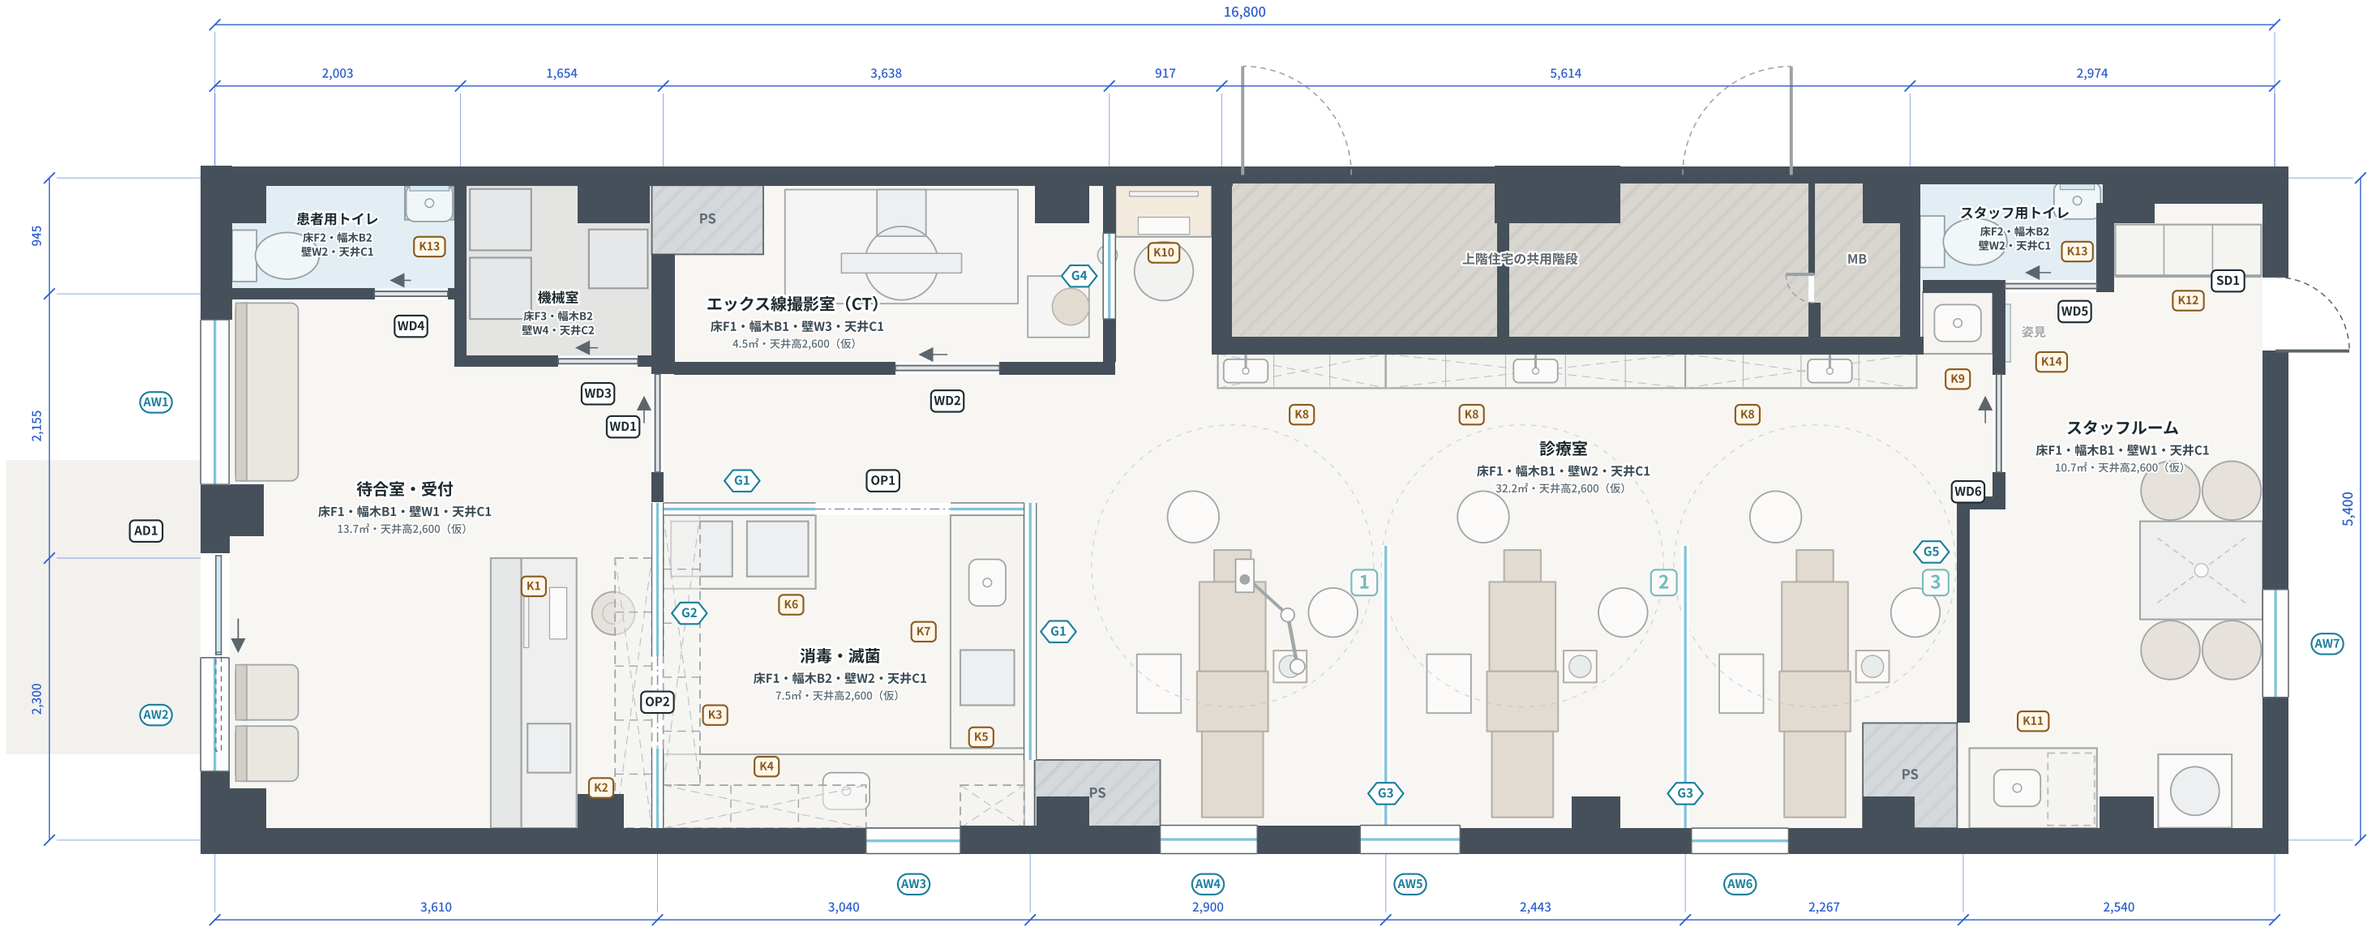

床F1　床F2　床F3　**WD1** 建具・開口（A-02）　**AW1** 窓（既存サッシ・A-02）　**G1** ガラス（A-02）　**K1** 造作家具・収納（A-04）　点線の四角＝吊戸棚・上部収納　家具は薄く表示

内装仕上表

室名	面積	床	幅木	壁	天井	天井高	備考
待合室・受付	13.7㎡	F1	B1	W1	C1	2,600（仮）	入口から全体を大理石調。受付の後ろのガラス壁の上に吊戸棚（K2）
患者用トイレ	1.4㎡	F2	B2	W2	C1	2,600（仮）	鏡・手洗い・換気扇。手すりの要否は相談
機械室	1.9㎡	F3	B2	W4	C2	2,600（仮）	コンプレッサー・バキューム。防音・防振。排気はダクトで外へ
エックス線撮影室（CT）	4.5㎡	F1	B1	W3	C1	2,600（仮）	壁・扉・操作窓に鉛（厚さは遮へい計算による）。使用中表示灯・標識
消毒・滅菌	7.5㎡	F1	B2	W2	C1	2,600（仮）	流し・作業台まわりはW5。換気扇（排気）。吊戸棚（K3・K4）
診療室（チェア1〜3・通路・画像PC・流し）	32.2㎡	F1	B1	W2	C1	2,600（仮）	チェアの配管のため床上げ（置床）か床下のピットが必要。壁面収納の作業台まわりはW5
スタッフ用トイレ	1.1㎡	F2	B2	W2	C1	2,600（仮）	鏡・手洗い・換気扇
スタッフルーム（通用口・ロッカー）	10.7㎡	F1	B1	W1	C1	2,600（仮）	ミニキッチンまわりはW5。洗濯機は防水パン。姿見（K14）
合計（目安）	**73.1㎡**	壁・柱・PSを除いた床の面積の合計（家具の下を含む）。寸法は現地の実測で確定					

仕上げ記号（見積の目安・品番は未定）

記号	部位	仕様
F1	床	大理石調 ビニル床シート（医療施設用・抗菌・耐薬品・防滑、継ぎ目は溶接）／色：白系 待合・受付は、大理石調の磁器質タイル（600角・防滑）も別途見積
F2	床	大理石調 ビニル床シート（トイレ用・耐水・防滑・抗菌）／色：白系
F3	床	ビニル床シート（グレー）＋機器の下に防振ゴム
B1	幅木	ソフト幅木 H60／色：薄いグレー
B2	幅木	床シートの巻き上げ H100（水まわり・掃除しやすく）
W1	壁	ビニルクロス（不燃・量産品）／色：白系
W2	壁	ビニルクロス（不燃・抗菌・汚れ防止、1000番台）／色：白系
W3	壁	鉛ボード下地＋ビニルクロス（W2） 鉛の厚さは、エックス線機器メーカーの遮へい計算による
W4	壁	遮音下地（遮音シート＋グラスウール充填）＋ビニルクロス（W1）
W5	壁	キッチンパネル（不燃化粧板・白） 流し・作業台・手洗いのまわり
C1	天井	石膏ボード＋ビニルクロス（不燃・白）
C2	天井	岩綿吸音板（白）

A-02 建具表・ガラス表・窓

建具表（室内の扉・開口）

記号	場所	形式	寸法	仕上げ	金物・備考
AD1	入口	自動ドア（片引き・窓側へ開く）	W857×H2,400	強化ガラス・アルミ枠（シルバー）	上の端を両側の窓（床から2,400）とそろえる。停電時は手で開く。既存開口の利用は要確認
WD1	診療室入口	片引き戸	W800×H2,000	化粧シート（白に近い薄いグレー）	ソフトクローズ・引手
WD2	エックス線撮影室	片引き戸	W850×H2,000	鉛入り・化粧シート（白に近い薄いグレー）	鉛の厚さは遮へい計算による。使用中表示灯・標識
WD3	機械室	片引き戸	W650×H2,000	防音仕様・化粧シート（白に近い薄いグレー）	鍵付き
WD4	患者用トイレ	片引き戸	W600×H2,000	化粧シート（白に近い薄いグレー）	表示錠（外から非常解錠）
WD5	スタッフ用トイレ	片引き戸	W750×H2,000	化粧シート（白に近い薄いグレー）	表示錠
WD6	スタッフルーム	引き込み戸（壁の中に引き込む）	W800×H2,000	化粧シート（白に近い薄いグレー）	戸が入る壁に姿見（K14）を付けるので、ビスの位置に注意
SD1	通用口	開き戸（既存）	W602（既存）	既存	既存利用。インターホン・電気錠は要否確認
OP1	消毒・滅菌（診療室通路側）	開口（扉なし）	W1,100×H2,000	—	開口の上は下がり壁
OP2	受付 → 消毒・滅菌	開口（扉なし）	W750×H2,000	—	開口の上を吊戸棚（K2・K3）が通る

ガラス表（間仕切り・特殊ガラス）

記号	場所	長さ	高さ・大きさ	すりガラス	種類・備考
G1	消毒・滅菌のガラス壁（通路側・チェア1側）	1,243・600・2,096	H2,600（天井まで）	床から1.3mまで	合わせガラス推奨（音対策）・枠なし。厚さは強度による
G2	受付の後ろのガラス壁（受付｜消毒・滅菌）	1,250・652	H2,000（その上は吊戸棚を支える下地の壁）	床から1.3mまで	合わせガラス推奨・枠なし
G3	チェアの間のガラス間仕切り（2か所）	2,302・2,302	H1,600	床から1.4mまで	強化ガラス・枠なし。ブース番号「1」「2」を彫刻
G4	エックス線の操作窓	—	W700×H1,000（床から800〜1,800）	—	鉛ガラス（厚さは遮へい計算による）
G5	ブース番号プレート「3」（チェア3の右の壁）	—	約W380×H440	全面	すりガラス・番号を彫刻

すりガラスは、ガラス加工でもフィルムでも可（見積は両方あると助かります）。ガラスの厚さ・合わせガラスの構成は、大きさと強度に合わせてご提案ください。

窓（既存サッシ）


記号	場所	幅	計画
AW1	待合（入口の左）	W1,343	既存のまま（床から50〜2,400）
AW2	入口の右（自動ドアが重なる側）	W927	既存のまま（床から50〜2,400）
AW3	消毒・滅菌	W769	高窓に（床から約1,970〜2,400）
AW4	チェア1	W792	高窓に（床から約1,970〜2,400）
AW5	チェア2	W815	高窓に（床から約1,970〜2,400）
AW6	チェア3	W792	高窓に（床から約1,970〜2,400）
AW7	スタッフルーム	W880	高窓に（床から約2,000〜2,400）

AW3〜AW7は、上の端を約30cm上げ（2,100→2,400）、高さを今の3分の1にした高窓の計画です。外まわり（サッシ）の工事のため、管理組合・オーナーの了承が前提で、上の端を上げられるかは梁の位置しだいです。むずかしい場合の代わりの案として、**内側から壁で窓の下の部分をふさいで高窓に見せる方法**の見積もお願いします。


色と仕上げの考え方

- 床は入口から全体を白の大理石の見た目に（本物の大理石ではなく、薬品・水に強い床シートを基本に）
- 壁・天井は白系。室内の引き戸は白に近い薄いグレー。受付カウンターは薄いグレー。チェア・イスはグレージュ
- 品番は未定です。量産品・1000番台などの等級で見積をお願いします（色・柄はサンプルで決定）
- 天井高2,600は仮です。梁・ダクト・配管のスペースを現地で確認して決めます
- エックス線撮影室の鉛の厚さは、機器メーカーの遮へい計算書によります（保健所への届出にも使用）
- すりガラスの高さは、消毒・滅菌まわり（G1・G2）が床から1.3m、チェアの間（G3）が床から1.4m


ガラス・建具の高さ（立面の略図・1/50）

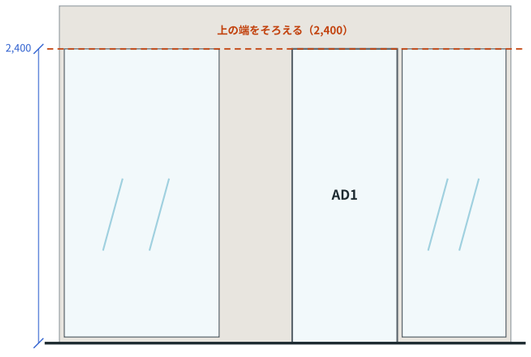


入口（外から）
AW1・AD1・AW2

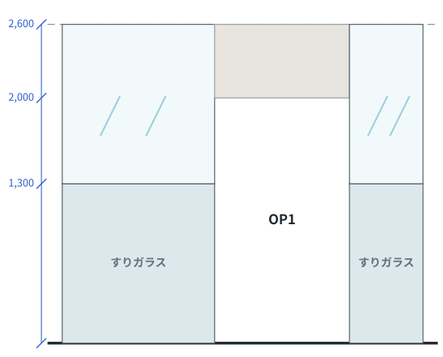


G1 消毒・滅菌のガラス壁
通路側から（OP1は扉なし）

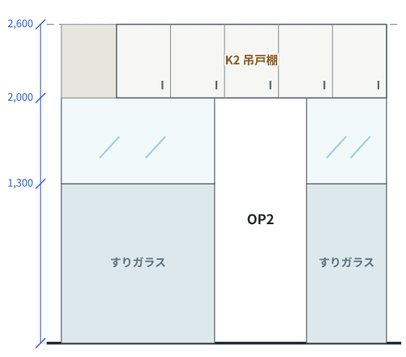

G2 受付の後ろの壁
受付側から（反対側にK3）

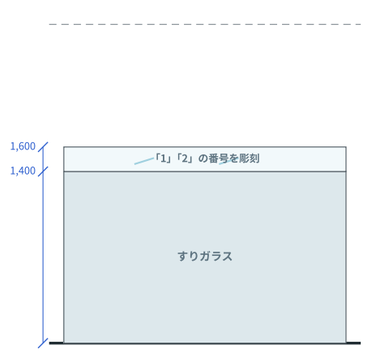


G3 チェアの間の間仕切り
2か所・枠なし

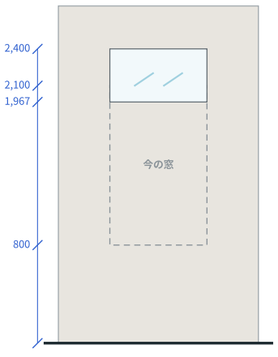

高窓（AW3〜AW7）
例：チェア1・外壁の内側から

A-03 設備配置図（給排水・歯科配管・電気・空調・換気）案

中葛西 歯科医院（仮称）内装工事　計画段階の案（見積用）
もとにした案：翔案（2026.11.03）　縮尺：1/50（A3）　作成：2026.11.03

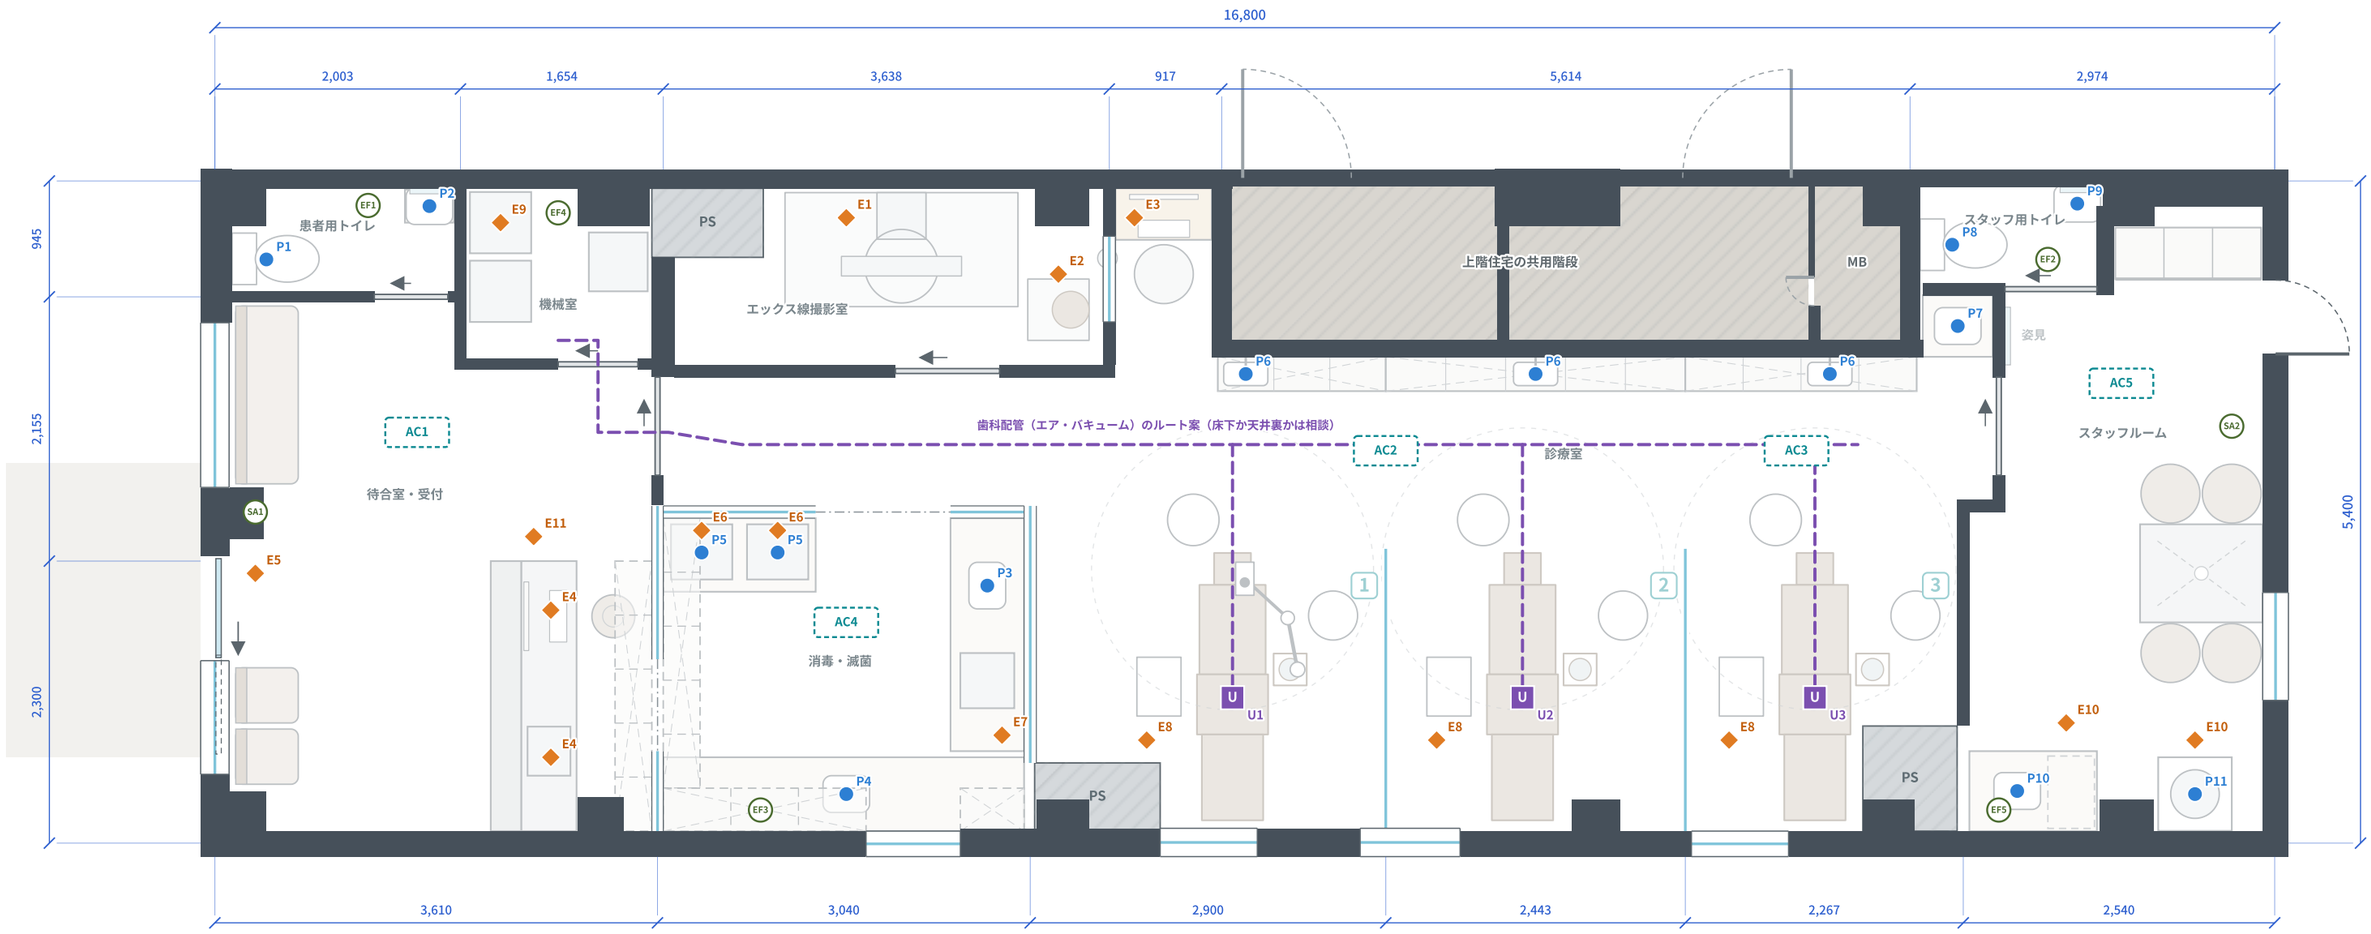

● 給水・排水

記号	場所	必要なもの
P1	患者用トイレ 便器	給水・排水
P2	患者用トイレ 手洗い	給水・排水
P3	消毒・滅菌 洗い場（K7）	給水・給湯・排水
P4	消毒・滅菌 流し（K5）	給水・給湯・排水
P5	オートクレーブ 2台	給水・排水（機種による・要確認）
P6	手洗い（壁面収納K8・3か所）	給水・排水（給湯は要否確認）・水栓の電源
P7	印象・石膏の流し（K9）	給水・排水（石膏トラップ）
P8	スタッフ用トイレ 便器	給水・排水
P9	スタッフ用トイレ 手洗い	給水・排水
P10	ミニキッチン 流し（K11）	給水・給湯・排水
P11	洗濯機	給水・排水（防水パン）

◆ 電源・LAN（主なもの）

記号	場所	必要なもの
E1	CT	専用回路（電圧・容量は機器メーカー指定）
E2	口内法エックス線	専用回路
E3	画像PC・エックス線の操作（K10）	コンセント・LAN
E4	受付（PC・プリンター・レセコン・カード端末）	コンセント・LAN（2か所）
E5	自動ドア	電源
E6	オートクレーブ 2台	専用回路（機種により200V）
E7	超音波洗浄器	コンセント
E8	各チェアのモニター・PC	コンセント・LAN
E9	コンプレッサー・バキューム（機械室）	専用回路（機種により200V・三相）
E10	スタッフルーム（冷蔵庫・電子レンジ・洗濯機）	コンセント（洗濯機はアース付き）
E11	Wi-Fi・ネットワーク機器	コンセント・LAN（置き場所は相談）

U 歯科ユニット（床のボックス）

記号	場所
U1	チェア1（マイクロスコープ付き）
U2	チェア2
U3	チェア3

各チェアに、給水・排水・エア・バキューム・電源（専用回路）。

AC 空調（室内機・案）

記号	場所
AC1	待合室・受付
AC2	診療室（チェア1・2）
AC3	診療室（チェア3）
AC4	消毒・滅菌
AC5	スタッフルーム

EF 換気

記号	場所
EF1	患者用トイレ 排気
EF2	スタッフ用トイレ 排気
EF3	消毒・滅菌 排気（外壁へ）
EF4	機械室 排気（ダクトで外へ）
EF5	ミニキッチン 排気
SA1	給気（待合）
SA2	給気（スタッフルーム）

紫の点線は、機械室から各チェアへの歯科配管（エア・バキューム）のルート案です（床下か天井裏かは相談）。位置はすべて案で、機器の電源・給排水は機器業者の設備要件図に合わせて決めます。照明と一般コンセントは、使い方に合わせてご提案ください。

造作家具・収納表／見積の前提と確認事項

造作家具・収納（K1〜K14）

記号	名前	大きさ（mm）	仕様・備考
K1	受付カウンター	W2,202×D700×H1,050（客側）／H720（机）	化粧板（薄いグレー）。配線の穴・コンセント・LAN。足元に収納
K2	吊戸棚（受付側）	W2,202×D300×H600（床から2,000〜天井）	扉5枚。出入口（OP2）の上も通る横一列
K3	吊戸棚（消毒・滅菌側・受付との壁）	W2,202×D300×H600（床から2,000〜天井）	扉5枚。オートクレーブの上も通るので湿気に強い面材。K4とL字につながる
K4	吊戸棚（消毒・滅菌・外壁側）	W1,654＋W520×D350×H1,100（床から1,500〜天井）	扉は上下2段。窓（AW3）の左右
K5	作業台・流し（消毒・滅菌・外壁側）	W2,943×D602×H850	シンク1（深型）・下部収納。まわりはキッチンパネル（W5）
K6	作業台（オートクレーブ置き）	W1,243×D600×H850	オートクレーブ2台（重さに耐える天板・専用コンセント）
K7	作業台・洗い場（チェア1側）	W600×D1,900×H850	シンク1・超音波洗浄器置き
K8	壁面収納（診療室・チェアの頭側・3台）	1,370・2,443・1,887×D280×H2,600（床〜天井）	下台（引き出し＋扉）、作業台H850、手洗い（各1・センサー水栓）、床から1,550〜天井は扉2段、手元灯
K9	印象・石膏の流し	W570×D502×H850	石膏トラップ付き
K10	画像PCの机（エックス線の操作）	W785×D420×H720	コンセント・LAN
K11	ミニキッチン（スタッフルーム）	W1,040×D652×H850	流し・下に小型冷蔵庫。まわりはW5
K12	ロッカー（通用口の横）	W1,190×D420×H2,400	3列×4段（12区画）
K13	トイレの手洗いと鏡（患者用・スタッフ用）	W400×D270・W300×D270×H800	鏡は手洗いの上（幅に合わせる・高さ約1,000）
K14	姿見（スタッフルームの出入口の横）	W470×H1,600（床から250〜1,850）	アルミ枠。引き込み戸の入る壁


家具（参考・別途購入の予定）

名前	内容	色
待合のベンチ	3人掛け・ひじ掛けなし・フラット（W約1,490）	グレージュ
待合のイス	2脚（入口の横・窓ぎわ）	グレージュ
受付の丸イス	1脚	グレージュ
スタッフルームの机	W1,000×D800・脚が中央から4方向に分かれるタイプ	薄いグレー
スタッフルームのイス	4脚	グレージュ
画像PCのイス	1脚	—

見積の前提と確認していただきたいこと


1. この図面は計画段階の案です（もとにした案：翔案）。寸法は既存図面（16,800×5,400・壁芯）からの想定で、現地の実測で確定します。
2. チェアの給水・排水・エア・バキュームの配管のため、診療室の床上げ（置床）か、床下のピットが必要です。方法・範囲・高さと、入口・トイレとの段差の解消（段差なしが希望）をご提案ください。
3. エックス線撮影室の遮へい（壁・扉・操作窓の鉛）は、機器メーカーの遮へい計算書によります。
4. 歯科ユニット・CT・コンプレッサー・バキューム・オートクレーブの電源・給排水は、機器業者の設備要件図に合わせます（チェアはタカラベルモント、マイクロスコープはチェア1に取り付け）。
5. 窓（AW3〜AW7）の高窓化は建物の外まわりの工事のため、管理組合・オーナーの了承が前提です。代わりの案（内側から窓の下をふさぐ）の見積もお願いします。
6. 上の階の共用階段・MBに面する壁は、防火区画の壁と考えています（要確認）。壁面収納（K8）の取り付けと手洗いの配管は、壁を貫通せず床から立ち上げる計画です。
7. 音・におい対策：機械室（コンプレッサー）は防音・防振。消毒・滅菌はガラス張りなので、超音波洗浄器・オートクレーブの音と消毒のにおいが受付・待合に届かないよう、換気と防音のご提案を。
8. 消防設備（自動火災報知設備・誘導灯・消火器など）は、所轄の消防署との協議によります。
9. 家具（左下の表）は別途購入の予定です。内装工事に含めるかは相談させてください。
10. 見積は、工事の区分（建物側の工事と内装工事の分け方）と、残す既存設備（エアコン・照明など）を確認のうえでお願いします。

壁面収納・受付まわりの略図（1/50）

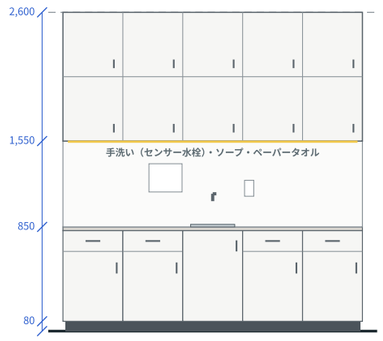


K8 壁面収納（例：チェア2・幅2,443）

正面から・奥行き280・床から天井まで

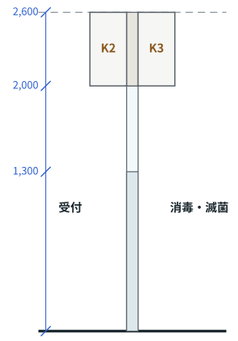

受付の後ろの壁（断面）

吊戸棚K2・K3は奥行き各300

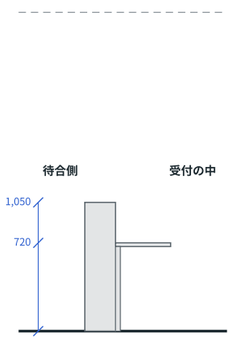

K1 受付カウンター（断面）

奥行き700（客側250・机450）