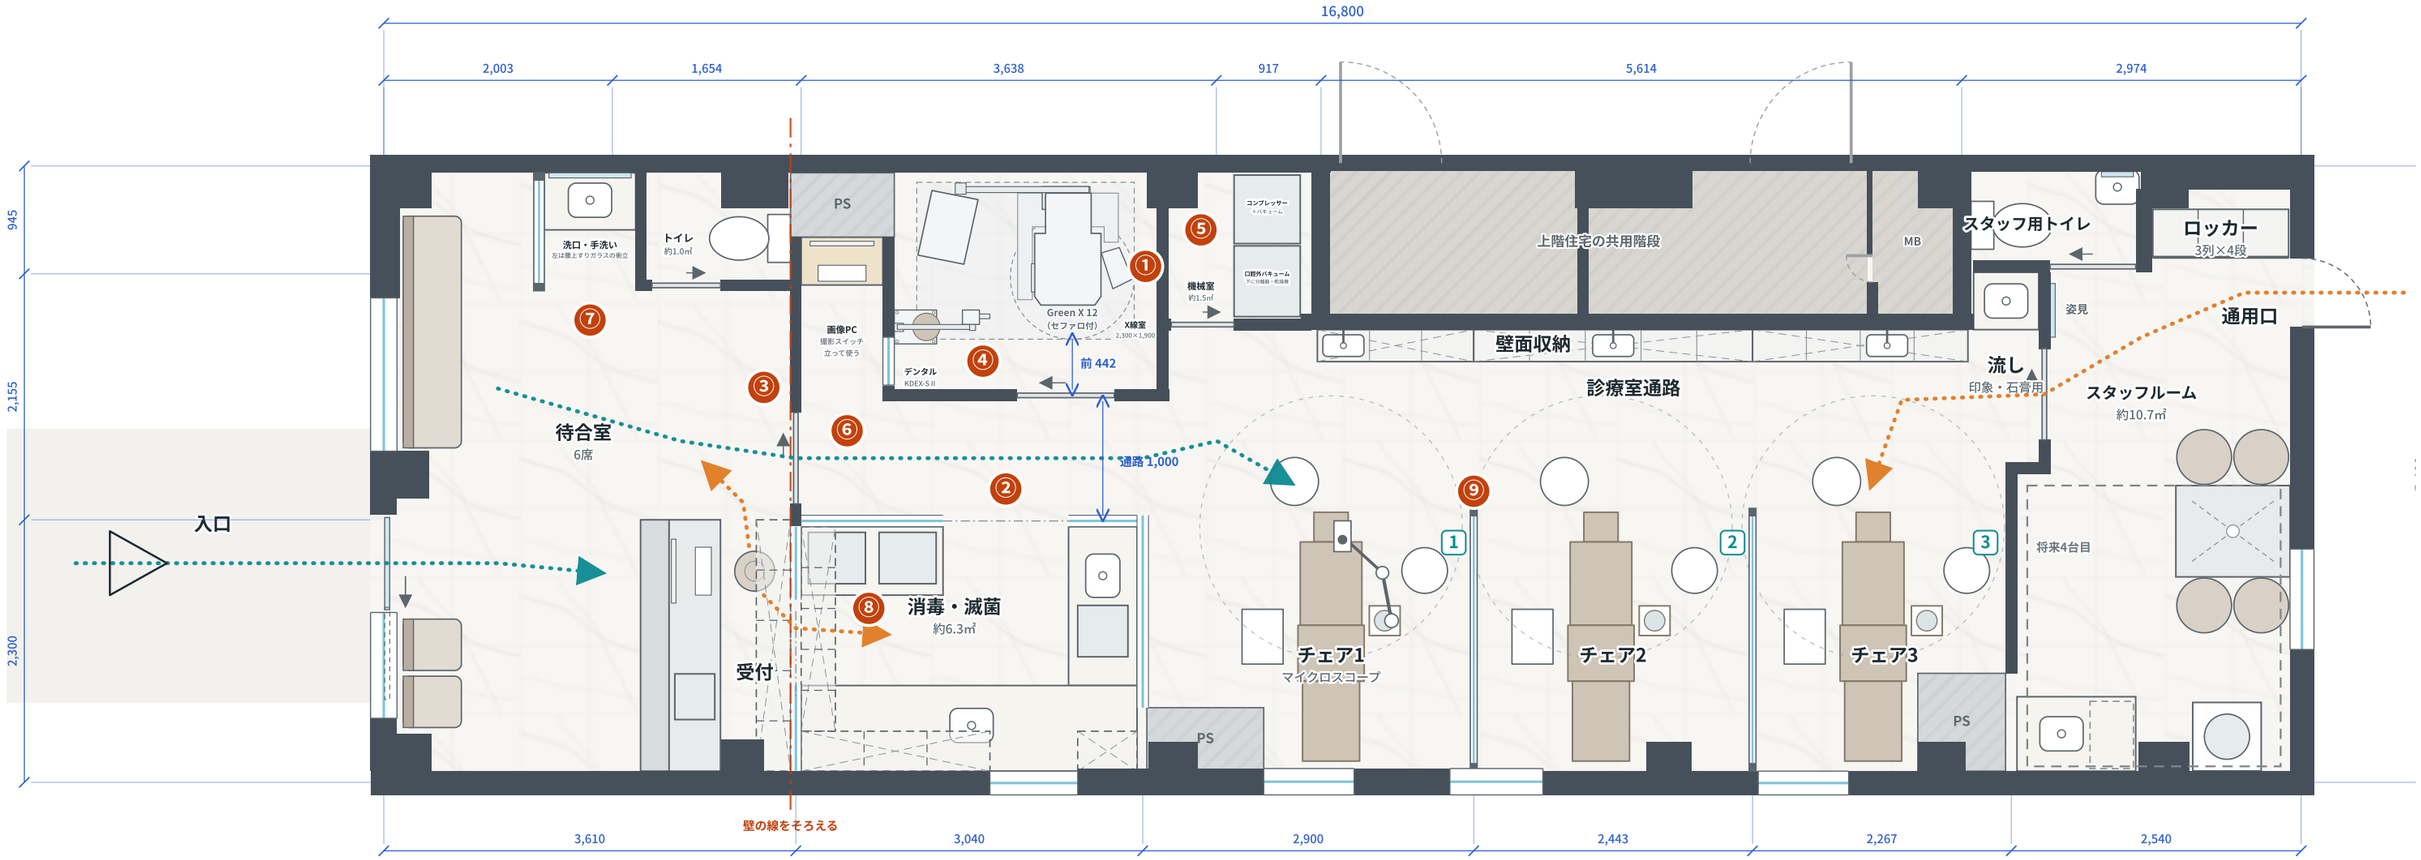


翔案5からの変更点

① エックス線撮影室の奥行きを1.44m→1.90mに、幅は2.3mに（推奨2,300×1,900・約4.3㎡）。CTはバテック Green X 12（セファロ付・セファロは左）。回る範囲の前から壁まで約44cm

② 通路の幅1.0mを残すため、消毒・滅菌の前の壁を約0.41m下げた（消毒・滅菌 約7.5㎡→約6.3㎡）

③ 診療室入口も、通路に合わせて約0.56m下へ（幅0.8m）

④ デンタル（KDEX-S II）は背中を左の壁につけ、患者さんは右を向いて座る。廊下側の壁から約40cm離し、頭の左右に約54cmずつあけた。セファロを撮るときはアームをよける

⑤ 機械室はX線室の右に、縦積みでコンパクトに（約1.5㎡）。コンプレッサーとバキュームを縦に積み、口腔外バキューム本体の台の下に分離器と乾燥機。空いた分で通路の入口を広げた

⑥ 画像PCと撮影スイッチは元の機械室の右半分（PSの下・約1.0㎡）。イスなしで立って使う（台の高さ約1,000）。X線室の確認用の窓は手前側に（デンタルの柱をよけて・幅約42cm）。トイレから受付までの壁の線をまっすぐに

⑦ 患者用トイレは手洗いなし（約1.0㎡・便器はPS側）。扉は待合側の引き戸（洗面のすぐ横）。洗口・手洗い（洗面台1つ）はトイレの外で、左は腰上すりガラスの衝立（高さ約1.8m）。待合は6席

⑧ 消毒・滅菌の窓側の作業台を奥行き600→750に。受付からの通り口は約10cm上へずらした（幅0.75mのまま）

⑨ チェアの間のガラス間仕切りに枠をつけた（ぶつかっても割れにくく）

患者さんの動線
スタッフの動線
ガラス間仕切り（H1,600・下から1.4mすりガラス・枠つき）
壁・柱
[1] ブース番号（ガラスに彫刻）
ガラス壁（天井まで・下から1.3mすりガラス）
床：白の大理石（入口から全体）

翔案6B（X線室 推奨寸法）

翔案5から：X線室を推奨寸法 2,300×1,900 に・機械室と水まわりも見直し

中葛西の建物 16,800×5,400（壁芯）／2026.11.04／寸法 mm

0 1 2 3 4 5 m

共通：マイクロスコープはチェア1に取り付け（床置きなし）
共通：診療室・消毒滅菌・スタッフルームの窓は高窓（床から約2.0〜2.4m）
点線の四角は吊戸棚・上部収納（床から約1.5m以上）